
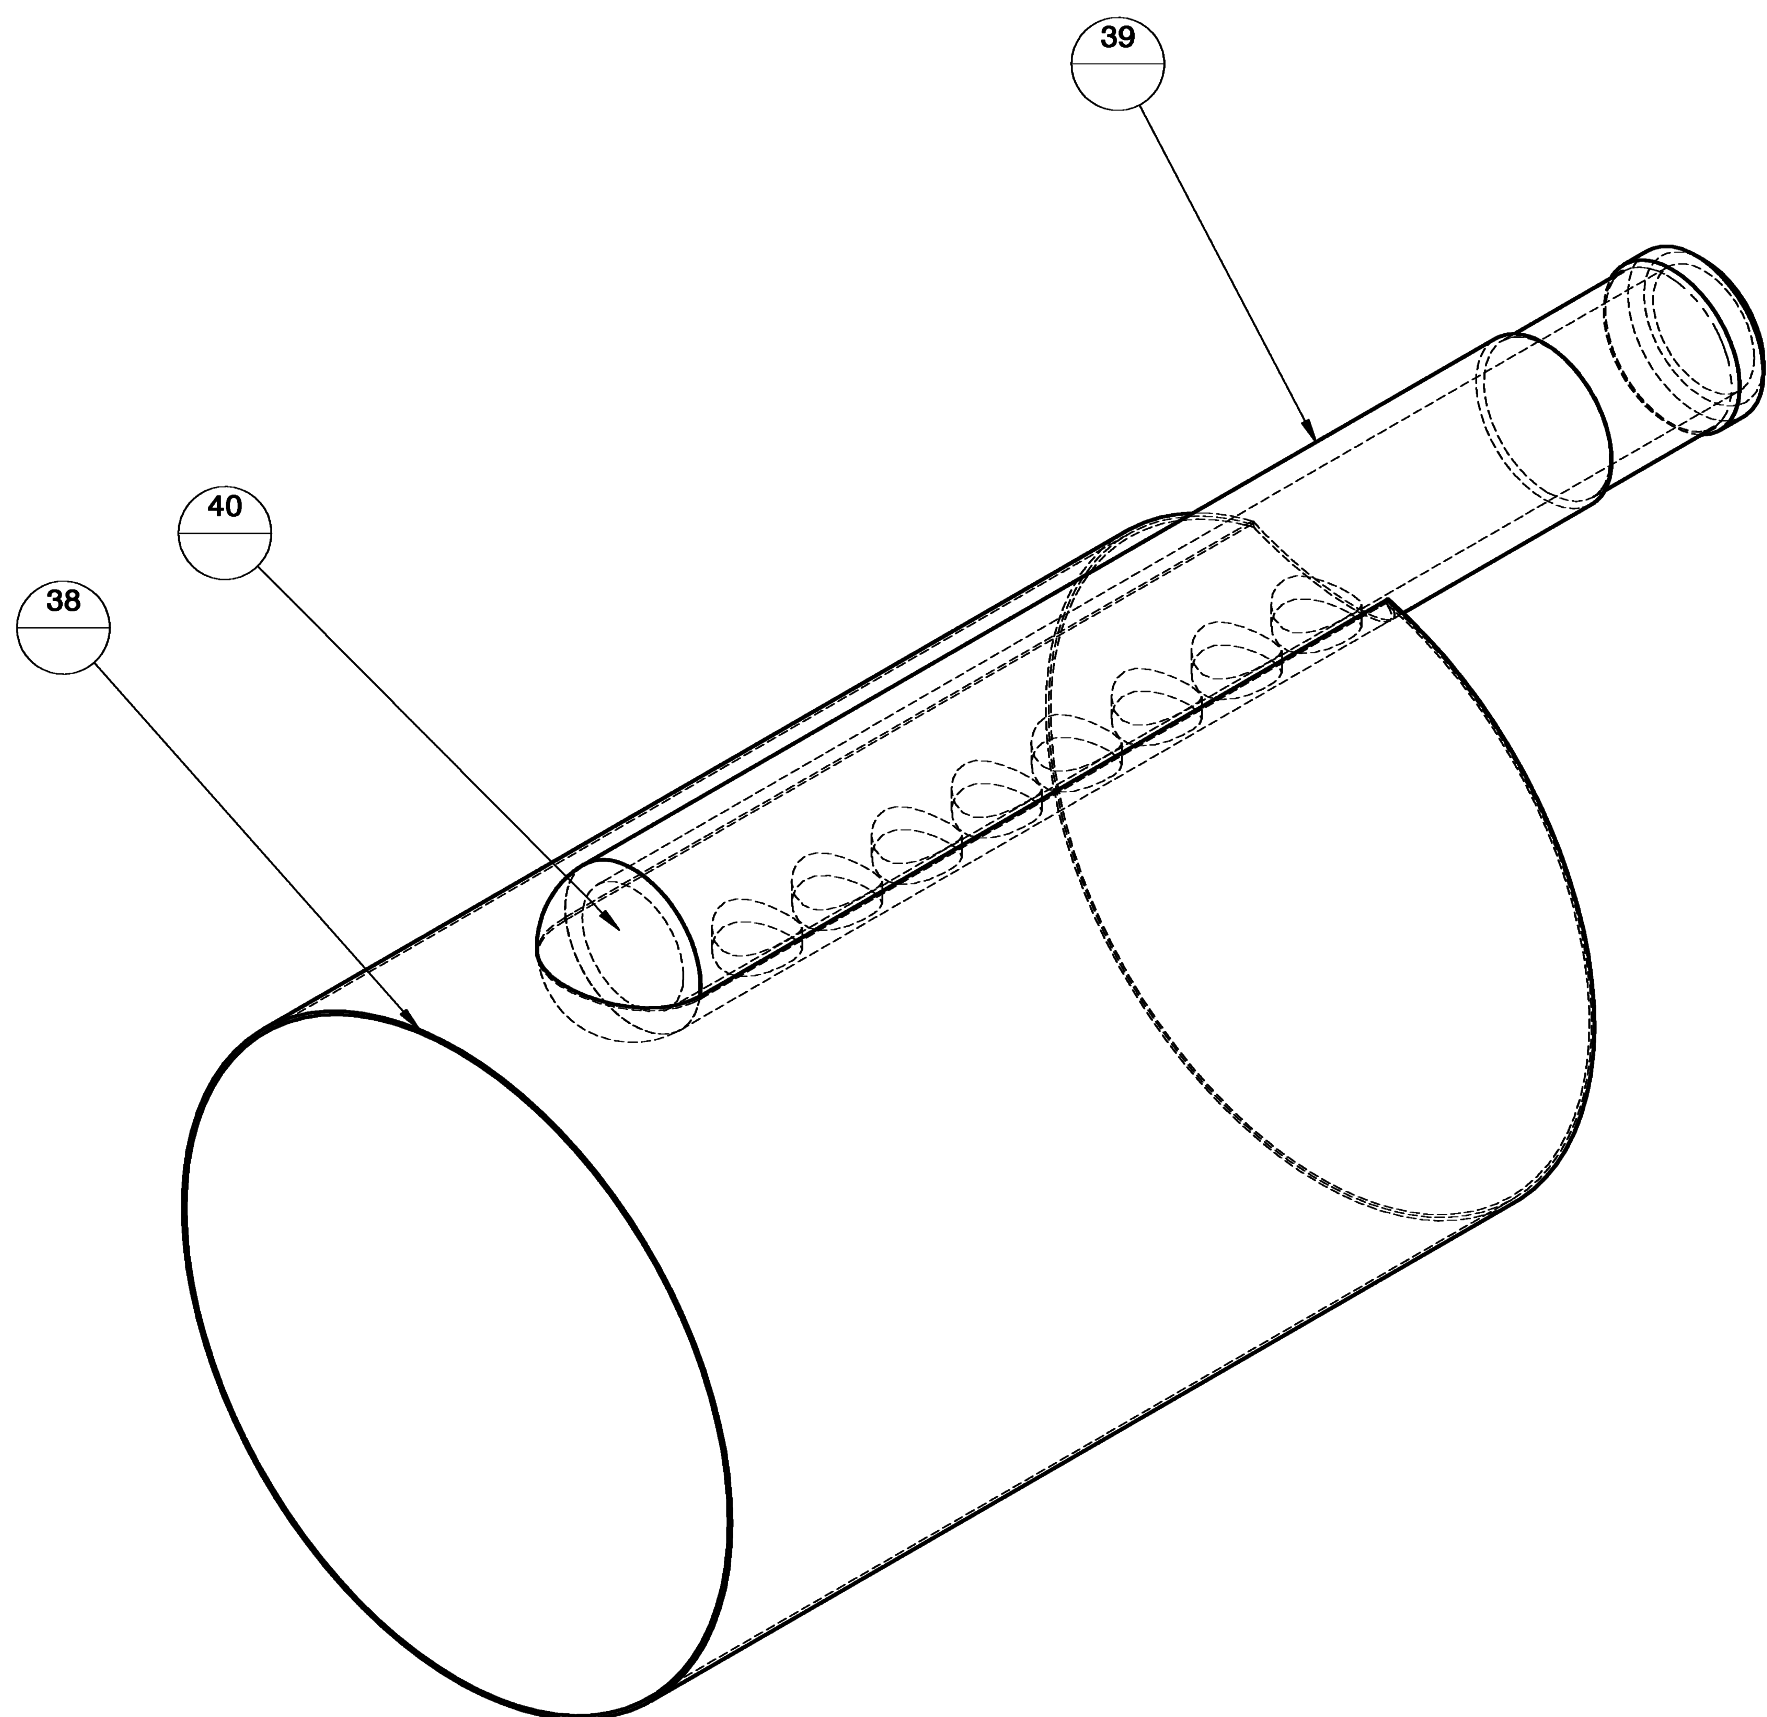
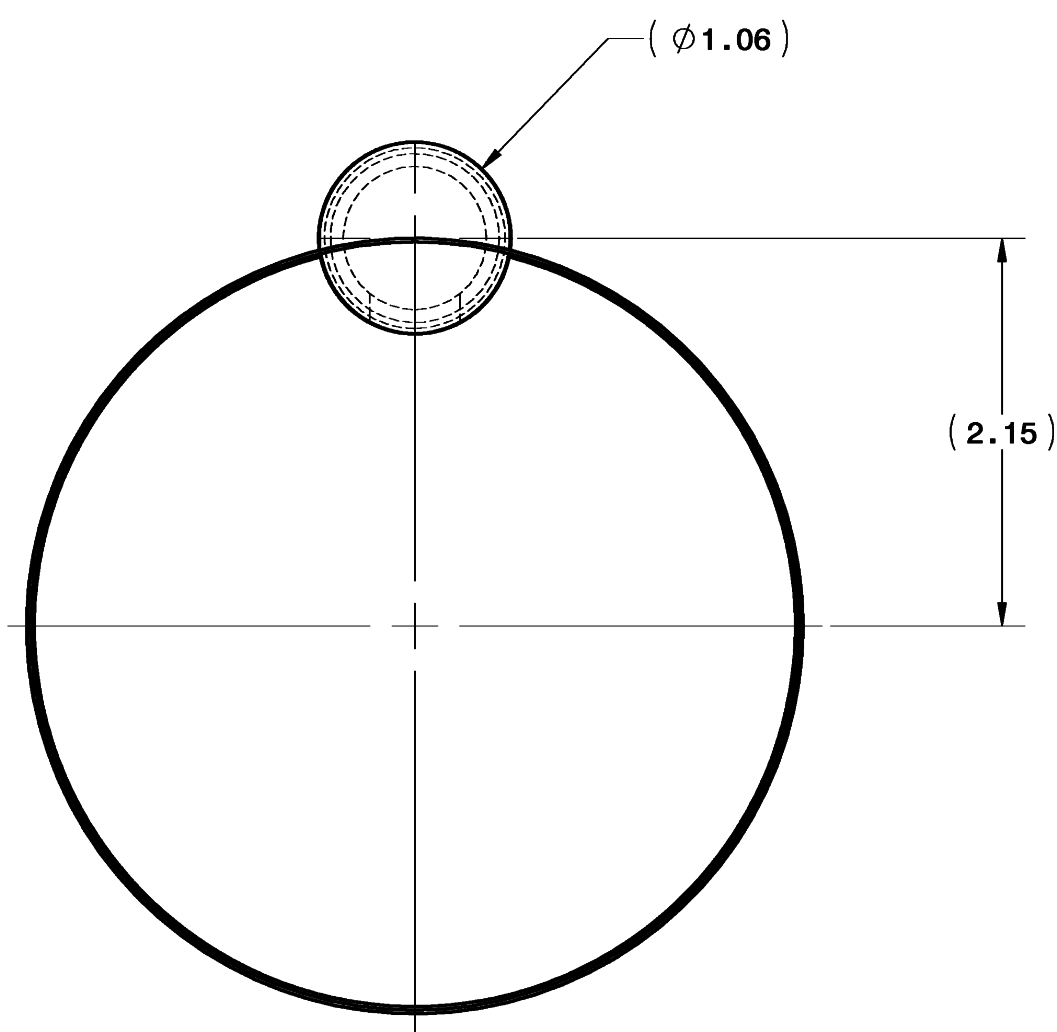


REV.	REVISION	DATE	BY
A	ITEMS 39, 40 SIZE CHANGED	7/14/2010	JASHWORTH
B	JOB DESCRIPTION CHANGE - PROJECT QUANTITY CHANGED FROM 3 TO 1.	7/27/2010	JASHWORTH

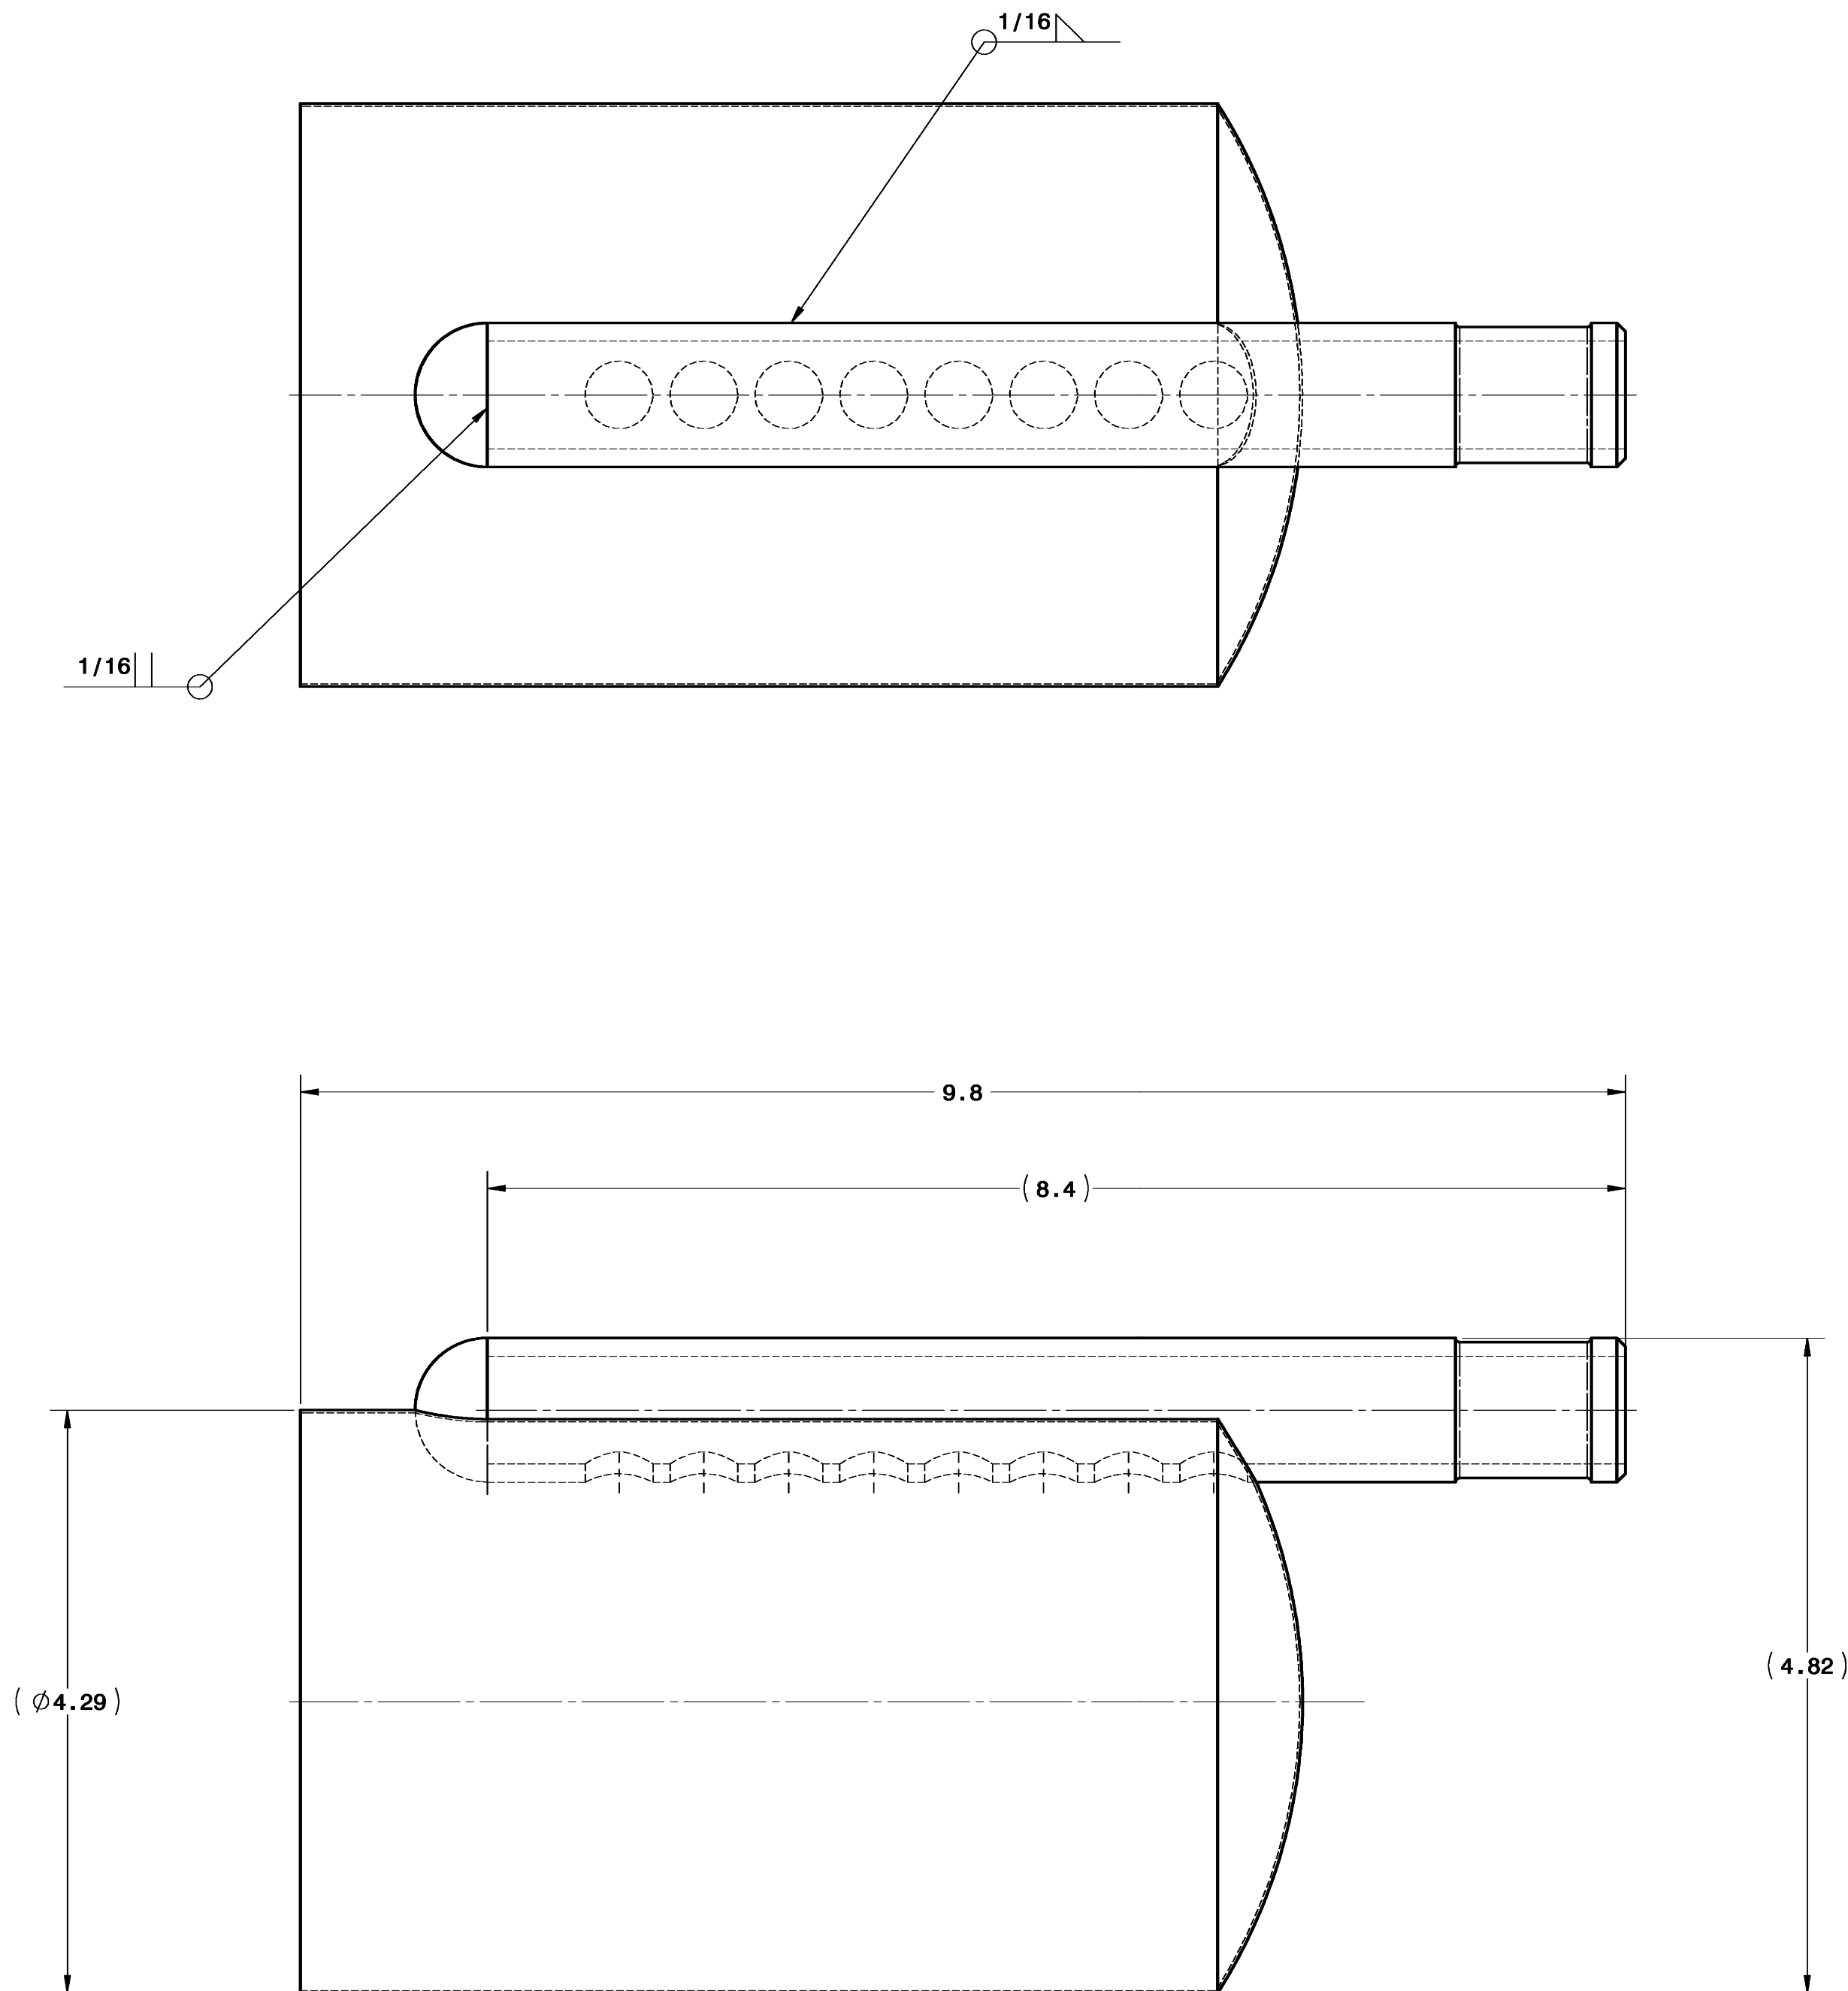

- NOTES:
1. ALL WELDS TO BE SPATTER AND SLAG FREE.
 2. ALL SURFACES TO BE OIL AND RUST FREE.
 3. WEIGHT: 1.5 LBS.
 4. TOLERANCES +/- 1/32".
 5. ALL WELDED CONNECTIONS MUST BE IN ACCORDANCE TO CSA-W59.
 6. WELD ITEMS 39 & 40 TOGETHER PRIOR TO WELDING TO ITEM 38
 7. PAINT NOTE:
-PAINT - SAFETY YELLOW
-PAINT TYPE - HIGH SOLIDS EPOXY
-PAINT PRODUCT # - 224
-MANUFACTURER - DEVCO COATINGS

ACCEPTED AS NOTED		ACCEPTED		NOT ACCEPTED	
Signature		Representing		Date	
J. Kien		gen		2010.09.17	
"The use and meaning of "ACCEPTED" is governed by the terms and conditions of the P.O. AECL Ref. No. 87630-223000 and in any event its use does not relieve the supplier of any of its obligations to AECL and/or its Client."					

ASSIGNED AECL NUMBER
RT-87630-71254-1035-1-DD-E Rev.0

BOM on Drawing For Reference Only			
00408	4	FILTER HOUSING PIPE CAP 1004 (USE ITEM)	USE ITEM 12995-1254-0040
00398	4	FILTER HOUSING TUBE 1004 (USE ITEM)	USE ITEM 12995-1254-0039
00380	4	FILTER HOUSING CANISTER 1004 (USE ITEM)	USE ITEM 12995-1254-0038
ITEM	QTY	DESCRIPTION	MFR
Material		Finish	Heat Treat
USE ITEM #1004		SEE DWG NOTE	NONE
QTY.	4	TOTAL	4
Drawing No. E-12995-1254-0035			
Rev. B			